

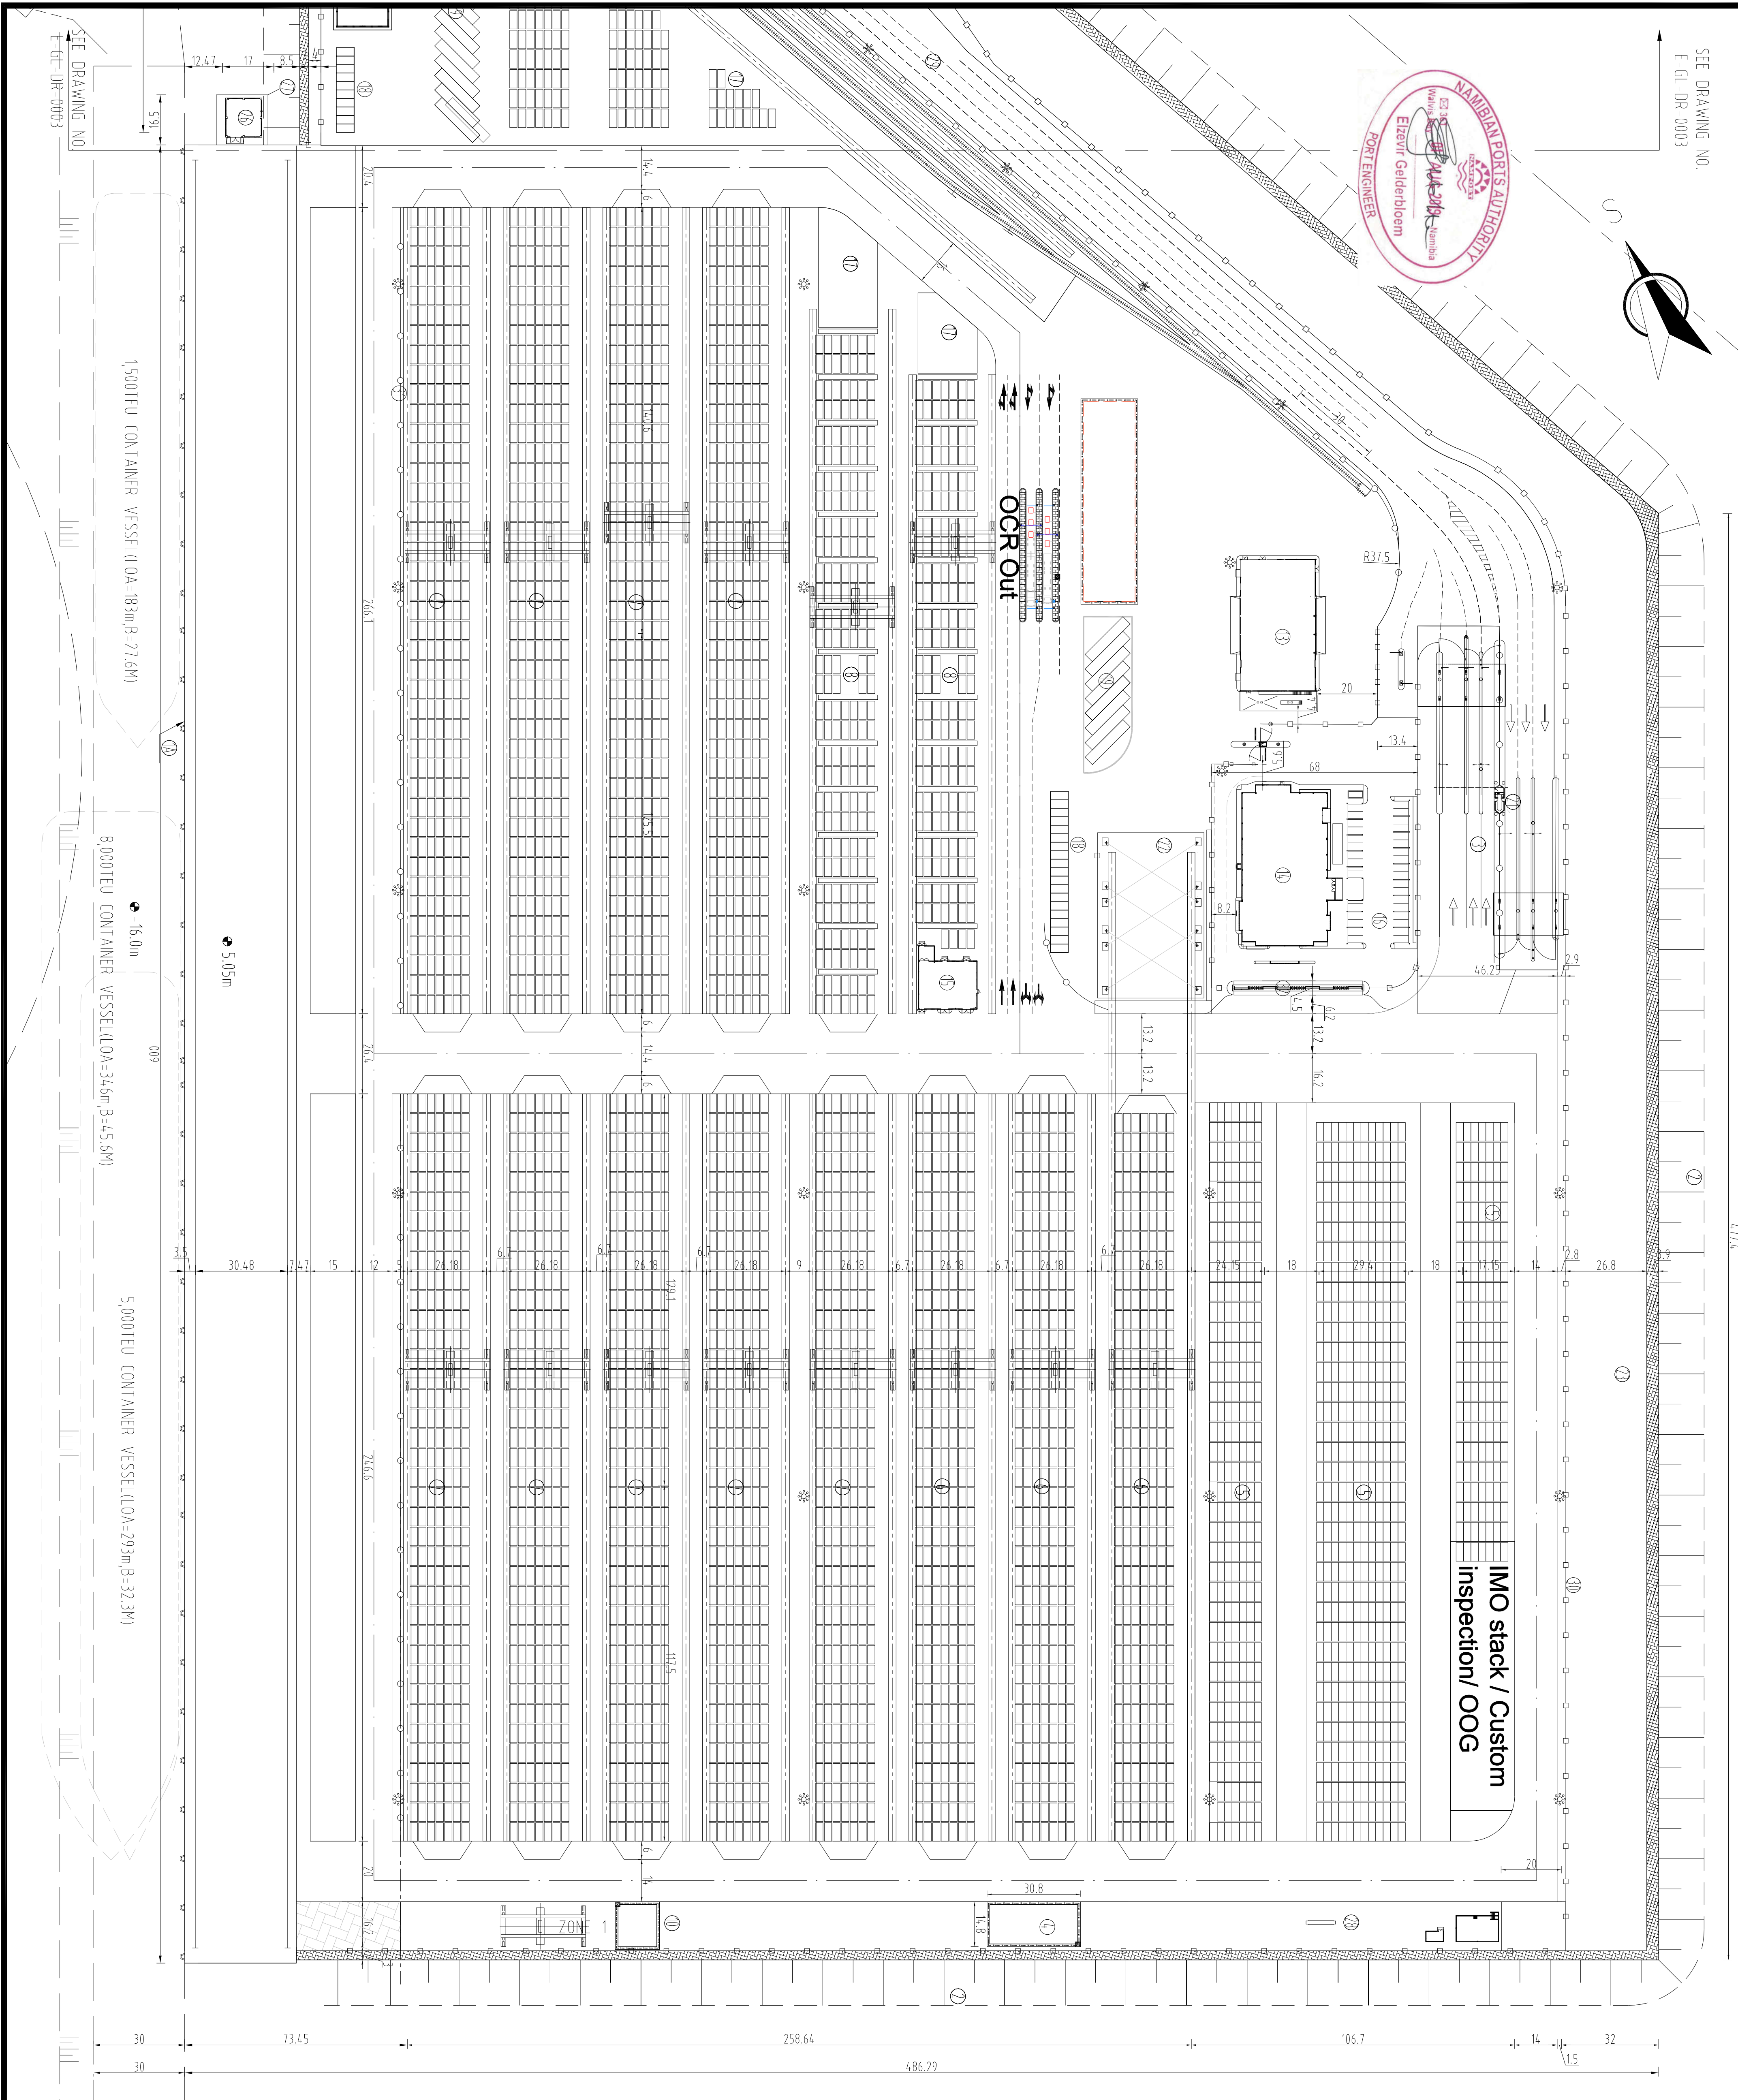


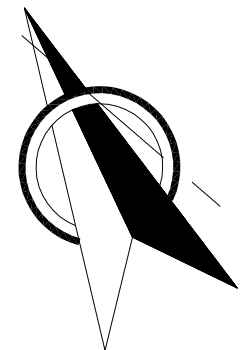

IMO stack / Custom
inspection/ OOG

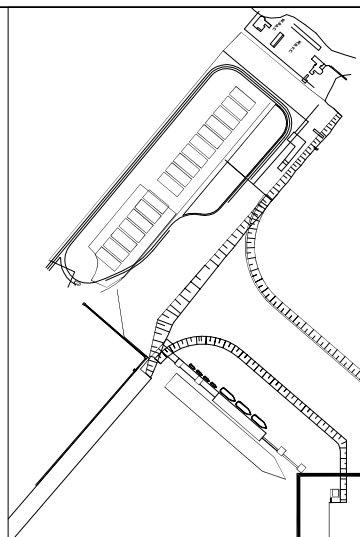

KEY PLAN

- NOTES:
1. ALL THE DIMENSIONS AND ELEVATIONS ARE IN METERS.
 2. THE ELEVATION IS REFERRED TO THE CD-LEVEL.
 3. THE COORDINATE SYSTEM IS REFERRED TO 1022/15 COORDINATE SYSTEM. THE RELATIONSHIP BETWEEN UTM AND 1022/15 COORDINATE SYSTEM IS AS BELOW:
 $X_{utm} = X_{cd} + (X_{maxcd} - X_{mincd}) \times K$
 $Y_{utm} = Y_{cd} + (Y_{maxcd} - Y_{mincd}) \times K$
($X_{cd} = 7567117.091$, $Y_{cd} = 499936.8028$, $K = 0.999610502$, $a = 3.1415625$)
 4. THE NUMBER OF PARKING LOTS CAN BE ADJUSTED BASED ON PRODUCTION STATUS.
 5. THE CONTROL POINTS OF BUILDINGS ARE THE INTERSECTION POINTS OF OUTER WALL AND GROUND.
 6. THE ITEMS SHOWN IN GREY DASH ARE NOT INCLUDED IN THE SCOPE OF WORK.

LEGEND:

- PROPOSED BERTH
RAIL FOR STS
LINE FOR RTG
LIGHTING
TRACTOR AND SEMI-TRAILER PARKING
BUS PARKING LOTS
EXISTINGS NEEDED TO BE DEMOLISHED
RTG
ROADMARKING
WIRELESS ACCESS POINT
- PALISADE FENCE
DIAMOND MESH FENCE
GRASS
TRACK
CAR PARKING LOTS
DIRECTION OF TRAFFIC
PORT ROAD
TUNNELS

GRAPHIC SCALE 0m 20m 40m 60m 80m

NO	DESCRIPTION	BY	CHK.	REV.	APP.
01	2019.08 FOR CONSTRUCTION	CA/WH	HIANG, W	YE/ J	SONG, L F
02	2019.04 FOR CONSTRUCTION	CA/WH	HIANG, W	YE/ J	SONG, L F
03	2018.08 FOR CONSTRUCTION	CA/WH	HIANG, W	YE/ J	SONG, L F
04	2018.06 FOR CONSTRUCTION	CA/WH	HIANG, W	YE/ J	SONG, L F
05	2018.06 FOR CONSTRUCTION	CA/WH	HIANG, W	YE/ J	SONG, L F
06	2017.10 FOR CONSTRUCTION	CA/WH	HIANG, W	YE/ J	SONG, L F
07	2016.11 FOR CONSTRUCTION	CA/WH	HIANG, W	YE/ J	SONG, L F
08	2015.09 FOR CONSTRUCTION	CA/WH	HIANG, W	YE/ J	SONG, L F

CLIENT:



NAMIBIAN PORTS AUTHORITY (NAMPOR)

PROJECT:

PORT OF WALVIS BAY NEW
CONTAINER TERMINAL ON RECLAIMED LAND

CONTRACTOR:



CHINA HARBOUR ENGINEERING COMPANY LTD.

TITLE:

TERMINAL LAYOUT
(SHEET 2 OF 3)

SCALE: 1:1000 DRAWN: CA/WH DATE: 2019.04 REV: db

DRAWING No. E-GL-DR-0004